


MENSURA

ESC. MENSURA 1:400-ESC. CALLES 1:1.000

VIAS DEL FERROCARRIL NACIONAL GENERAL BARTOLOME MITRE

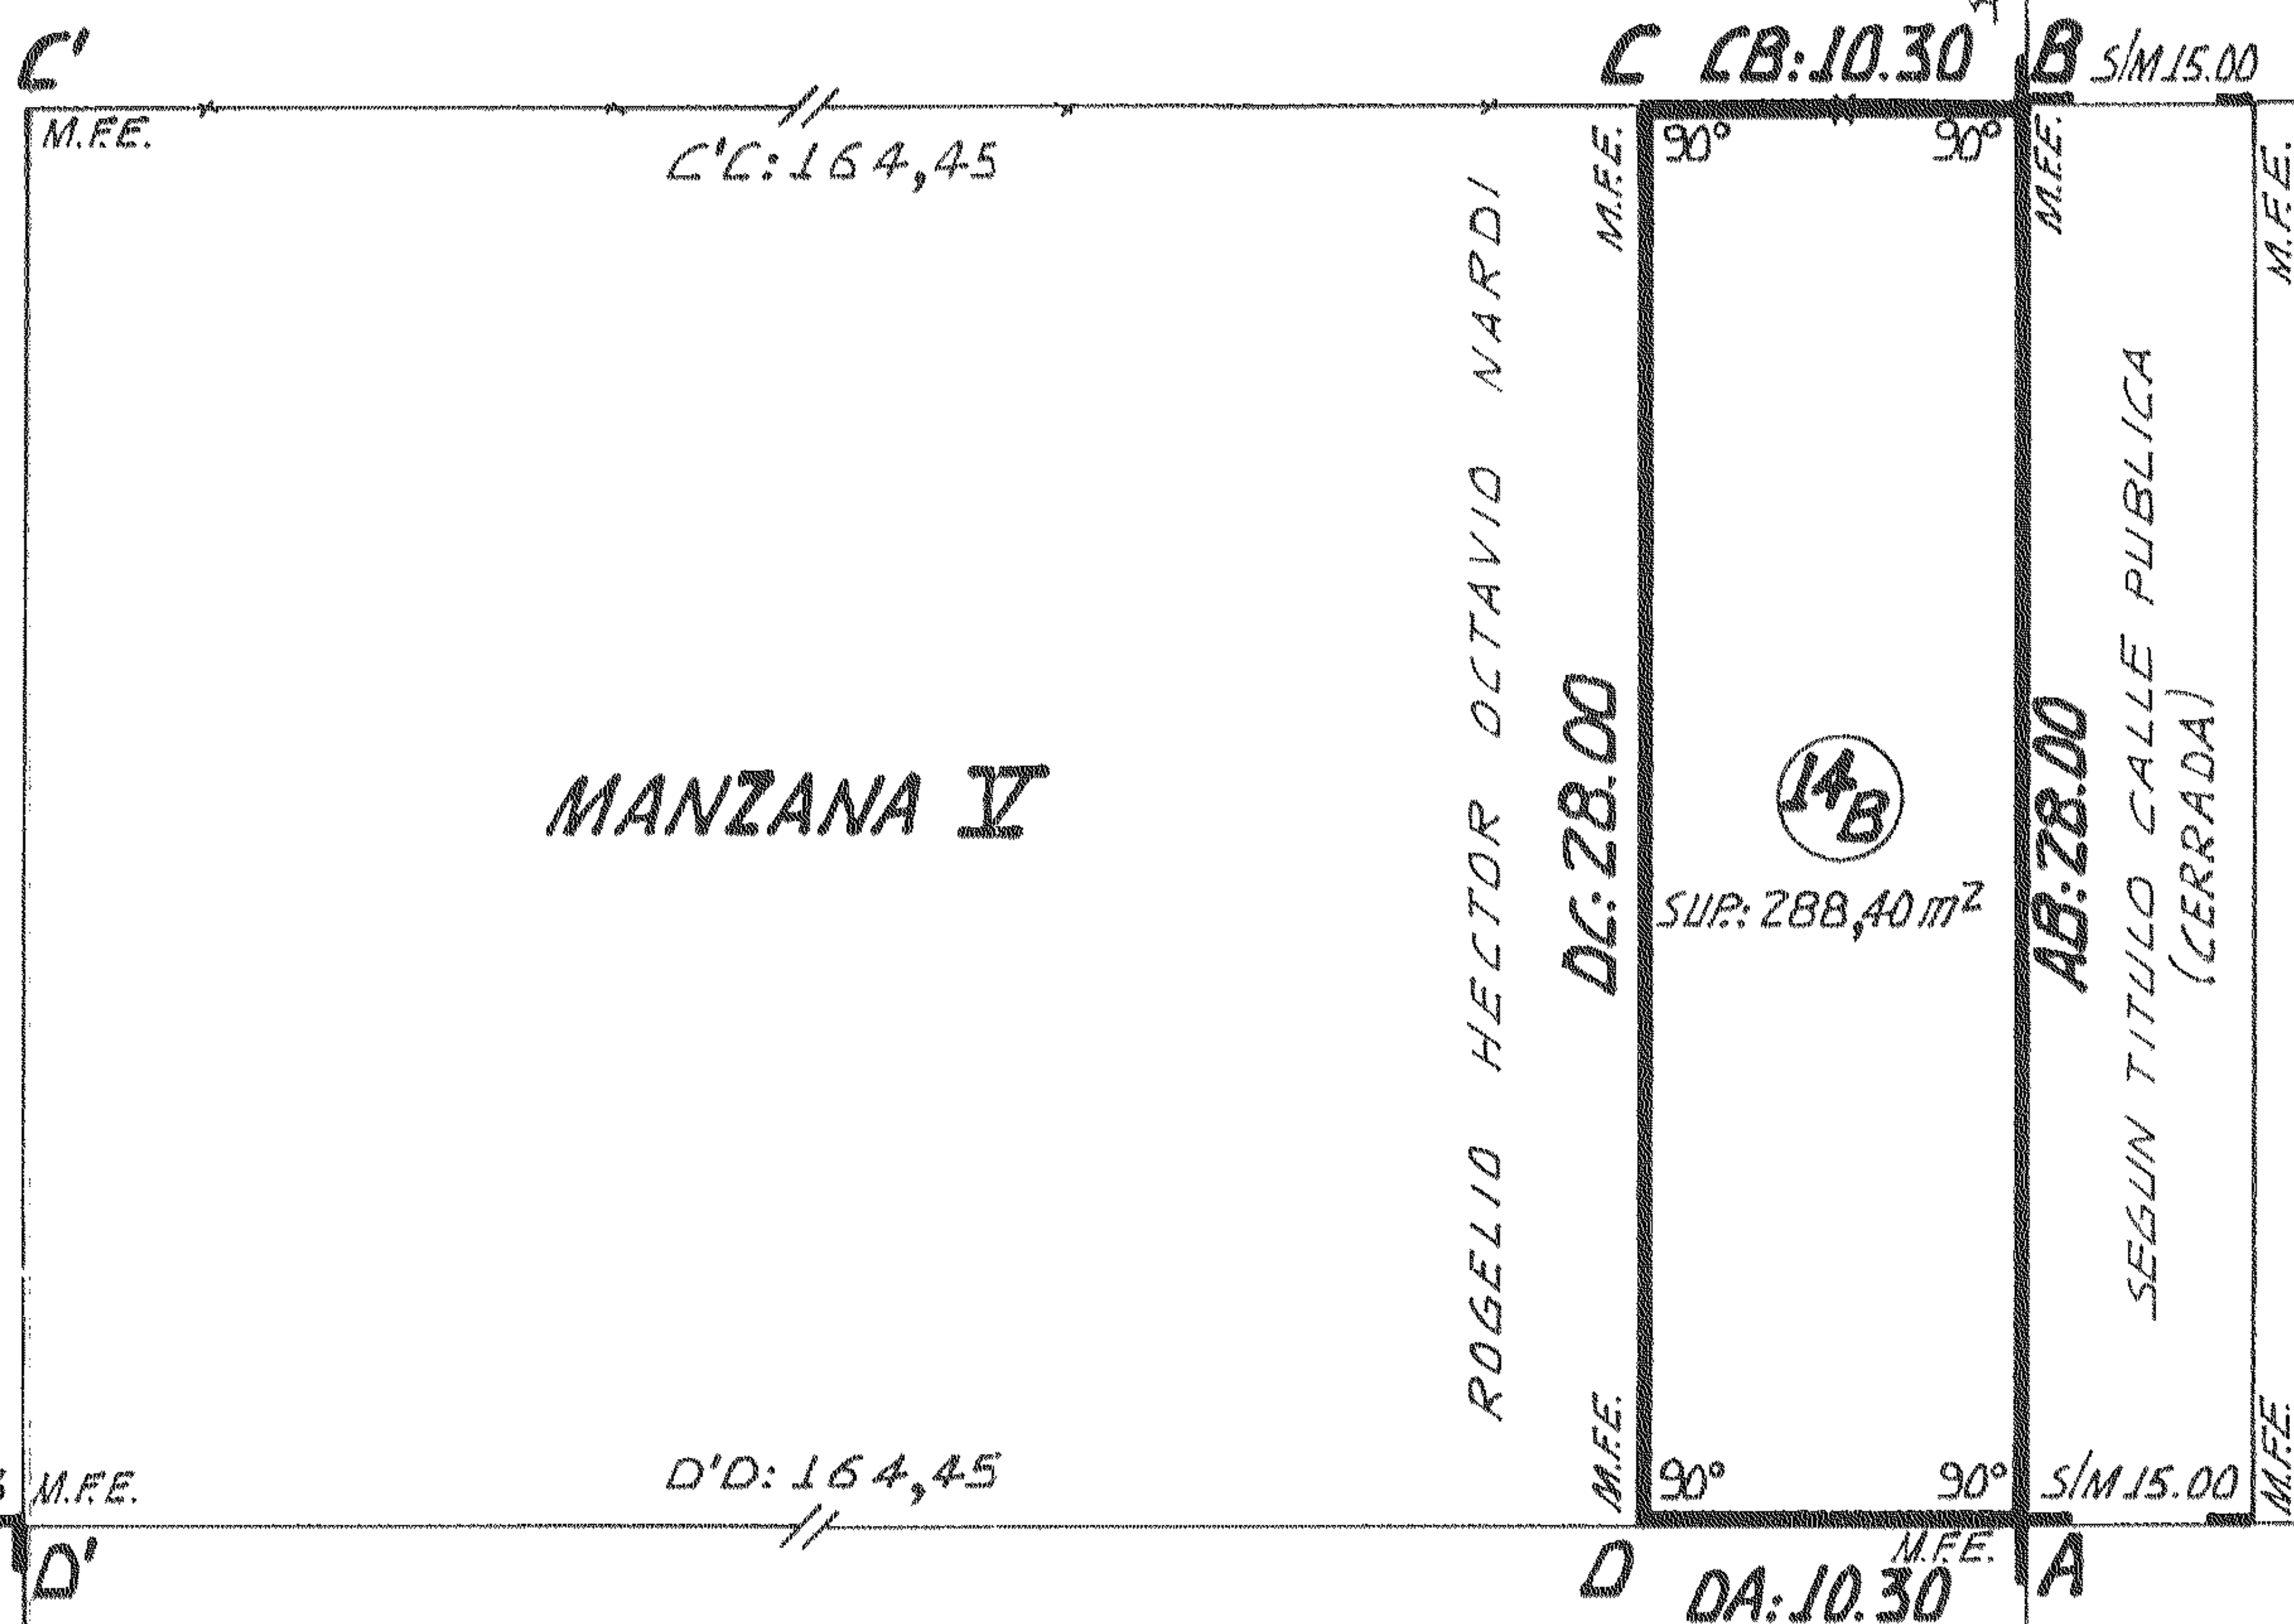


MANZANA V

LOT 14B
SUP: 288,40 m²

Boulevard BUENOS AIRES
A.O. 30.00

CROQUIS S/TITULO Y
PLANO N° 96.451/78. 2º de Orden.
ESCALA 1:500

VIAS DEL
FERROCARRIL CENTRAL
NACIONAL GENERAL
BARTOLOME MITRE

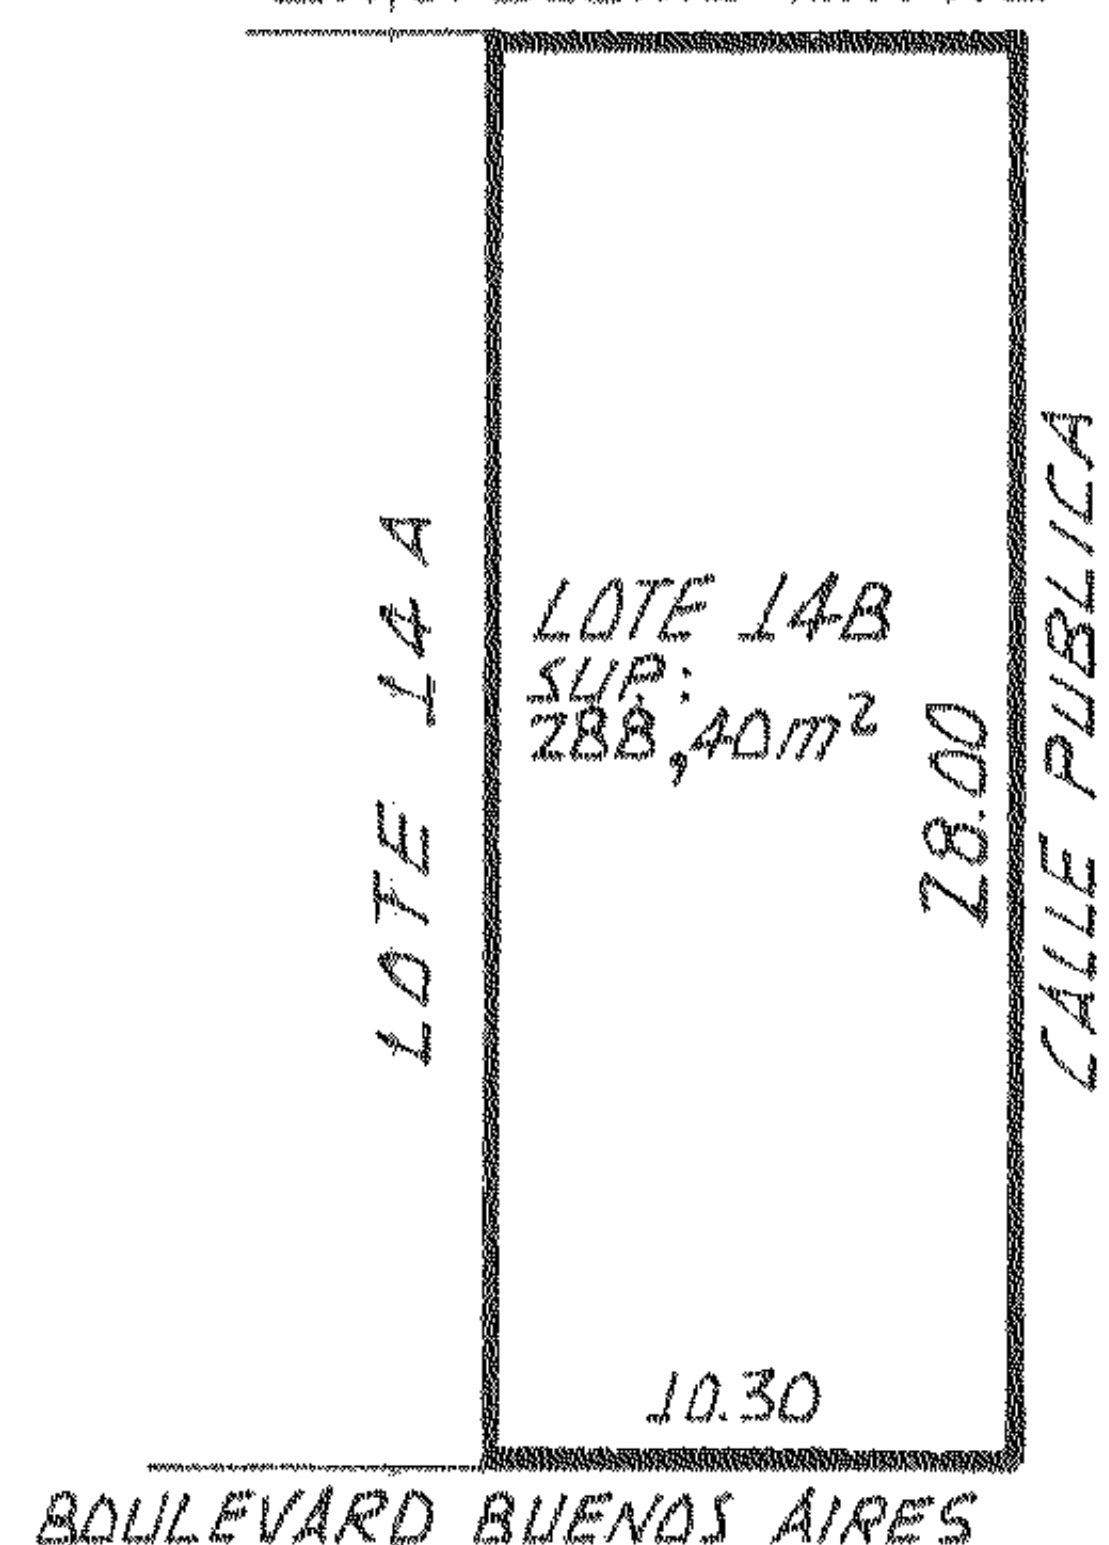

Dupl. 607 Caseros 129262/90. -

PROVINCIA DE SANTA FE
DEPARTAMENTO CASEROS
DISTRITO ARTEAGA
LUGAR PUEBLO ARTEAGA

PLANO N° 96.451/78

P.I. N° 393.370/0003

AV. TERR. \$2.0,0028-
AV. MEJ. \$2. ---
AÑO 1964

OBJETO

MENSURA PARA INFORMACION POSESORIA

POSEEDOR


ROGELIO HECTOR OCTAVIO NARDI

INMUEBLE: MANZANA V - LOTE 14B DEL PLANO 96.451/78

DOMINIO: T° F° N° AÑO:
DPTO. CASEROS

BALANCE DE SUPERFICIES

SUP. LOTE 14B-POLIGONO "ABCD" S/M 288,40 m²

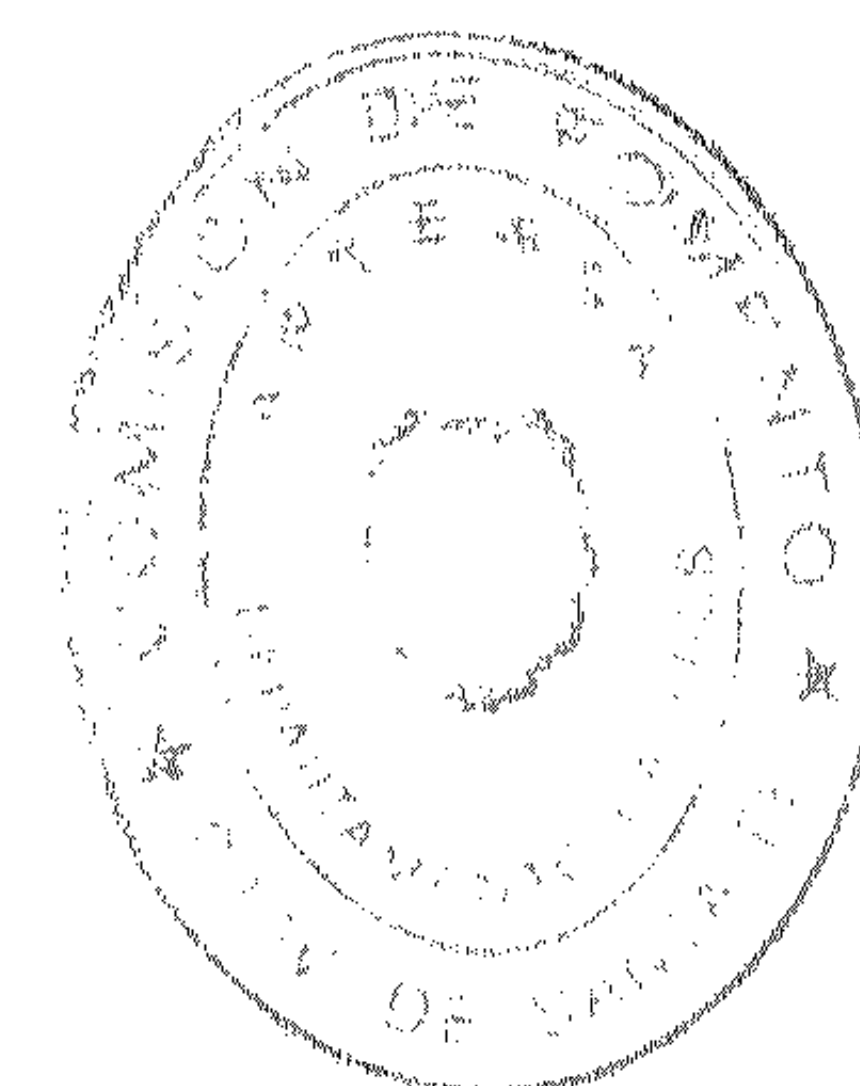

ING. GEOGRAFO ROBERTO D.S. DIAZ
I.C.I. 6101/19-SAN MARTIN 1967- CASILDA

CASILDA, ENERO 1986


OBSERVACIONES: S/M: SEGUN MENSURA - A.D. ANCHO OFICIAL.
MEDIDAS LINEALES EXPRESADAS EN METROS.
M.FE. MOJON HIERRO EXISTENTE.

EN LA NOTA DE DOMINIO T° 234-F° 260-N° 194754-AÑO 1983 EN EL 2º DE ORDEN-DEPARTAMENTO CASEROS, EL POSEEDOR ADQUIERE LOS DERECHOS Y ACCIONES DE LA FRACCION DESCRIPTA EN EL CROQUIS S/TITULO.

SUBSISTE DOMINIO AL T° 5 - F° 57.379 - N° 1365-13.082 A NOMBRE DEL ESTADO NACIONAL ARGENTINO

Ing. G. E. MAURIO
JEFE DEPARTAMENTO CASEROS
ROSARIO

NOMENCL. CATASTRAL

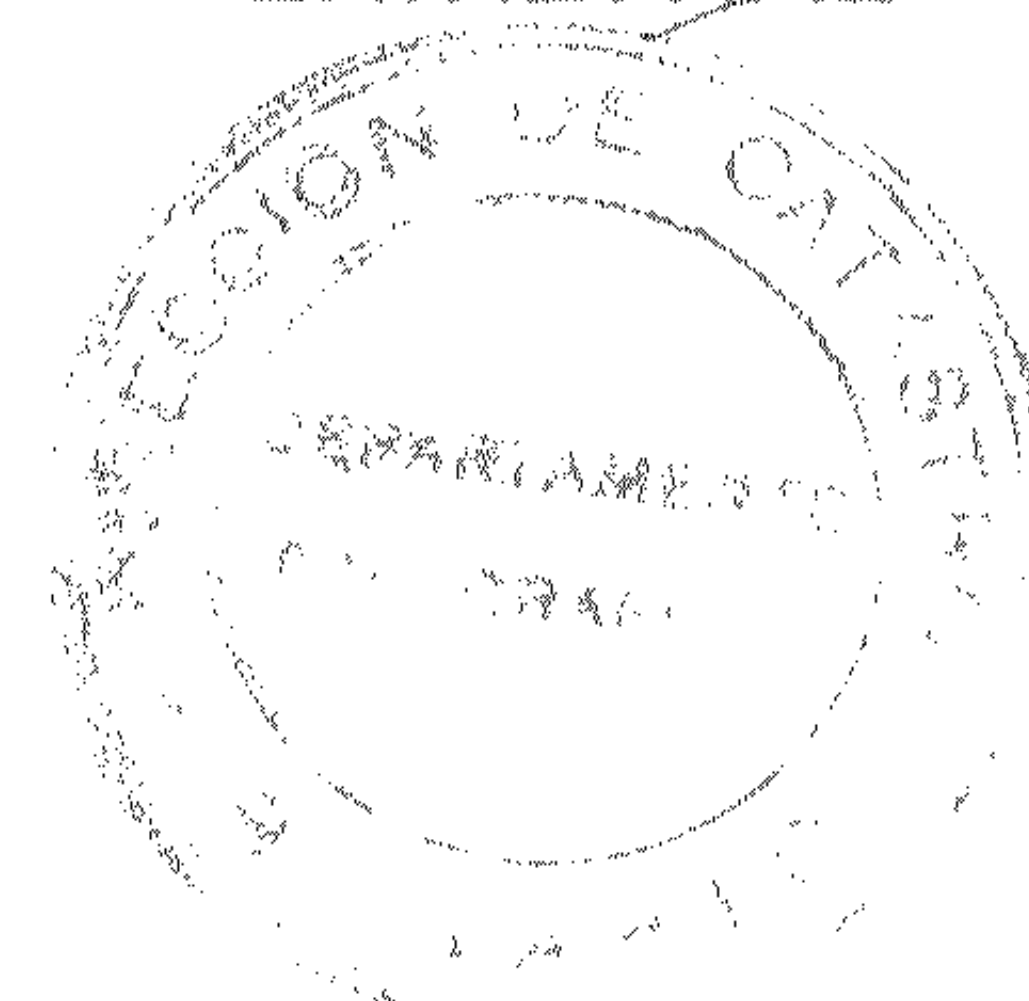

D. SANCIONADO POR ROSARIO

Dupl. 607 Caseros