96451/78

F.C.N.G.B.M.
ESTACION
I
II
III
IV
V
VI
14B
A
B
C
D
E
F
G
H
I
J
K
L
M
N
O
P
Q
R
S
T
U
V
W
X
Y
Z
12.50
28
100
60.14
18.20
12.25
13.58
10.30
14.70
QR: 174.75
TS: 174.75
Q'R': 2.20 RY: 4.70
T'S': 2.20 SZ: 4.70
UV: 89.70
XW: 89.70
BVRD. BUENOS AIRES
A.O. 30.-
S/M 15.00
S/M 29.75
S/M 14.75
S/M 29.76
S/M 14.76
S/M 29.87
S/M 14.87
S/M 30.-
S/M 25.85
S/M 19.92
MZA. 31
MZA. 30
MZA. 29
MZA. A
MZA. B
MZA. C
100
100.28
188
90
CALLE PARAGUAY A.O. 15.-
CALLE CHILE A.O. 15.-
CALLE URUGUAY A.O. 15.-
BV. SARMIENTO A.O. 20.-
BVRD. GRAL. SAN MARTIN
CALLE SANTA FE A.O. 15.-
CALLE H. IRIGOYEN A.O. 15.-
N

| **MZA. I** | |
|---|---|
| LOTES | SUPERFICIES m² |
| 1 | 350,00 |
| 2 | 350,00 |
| 3 | 350,00 |
| 4 | 350,00 |
| 5 | 350,00 |
| 6 | 350,00 |
| 7 | 350,00 |
| 8 | 350,00 |
| TOTAL S/M | 2800,00 |

| **MZA. II** | |
|---|---|
| LOTES | SUPERFICIES m² |
| 1 | 350,00 |
| 2 | 350,00 |
| 3 | 350,00 |
| 4 | 350,00 |
| 5 | 350,00 |
| 6 | 350,00 |
| 7 | 350,00 |
| 8 | 350,00 |
| TOTAL S/M | 2800,00 |

| **MZA V** | |
|---|---|
| LOTES | SUPERFICIES m² |
| 1 | 343,00 |
| 2 | 350,00 |
| 3 | 350,00 |
| 4 | 350,00 |
| 5 | 350,00 |
| 6 | 350,00 |
| 7 | 350,00 |
| 8 | 350,00 |
| 9 | 350,00 |
| 10 | 350,00 |
| 11 | 350,00 |
| 12 | 350,00 |
| 13 | 350,00 |
| 14A | 61,60 |
| TOTAL S/M | 4604,60 |

| **MZA. VI** | |
|---|---|
| LOTES | SUPERFICIES m² |
| 1 | 350,00 |
| 2 | 350,00 |
| 3 | 350,00 |
| 4 | 350,00 |
| 5 | 350,00 |
| 6 | 350,00 |
| 7 | 411,60 |
| TOTAL S/M | 2511,60 |

SUP. LOTE 14B 288,40 m²

TOTAL Mza. V 4893,00 m²

**MZA. III : 1683,92 m²  SUP. IV : 509,60 m²**

## CROQUIS S/TITULO I

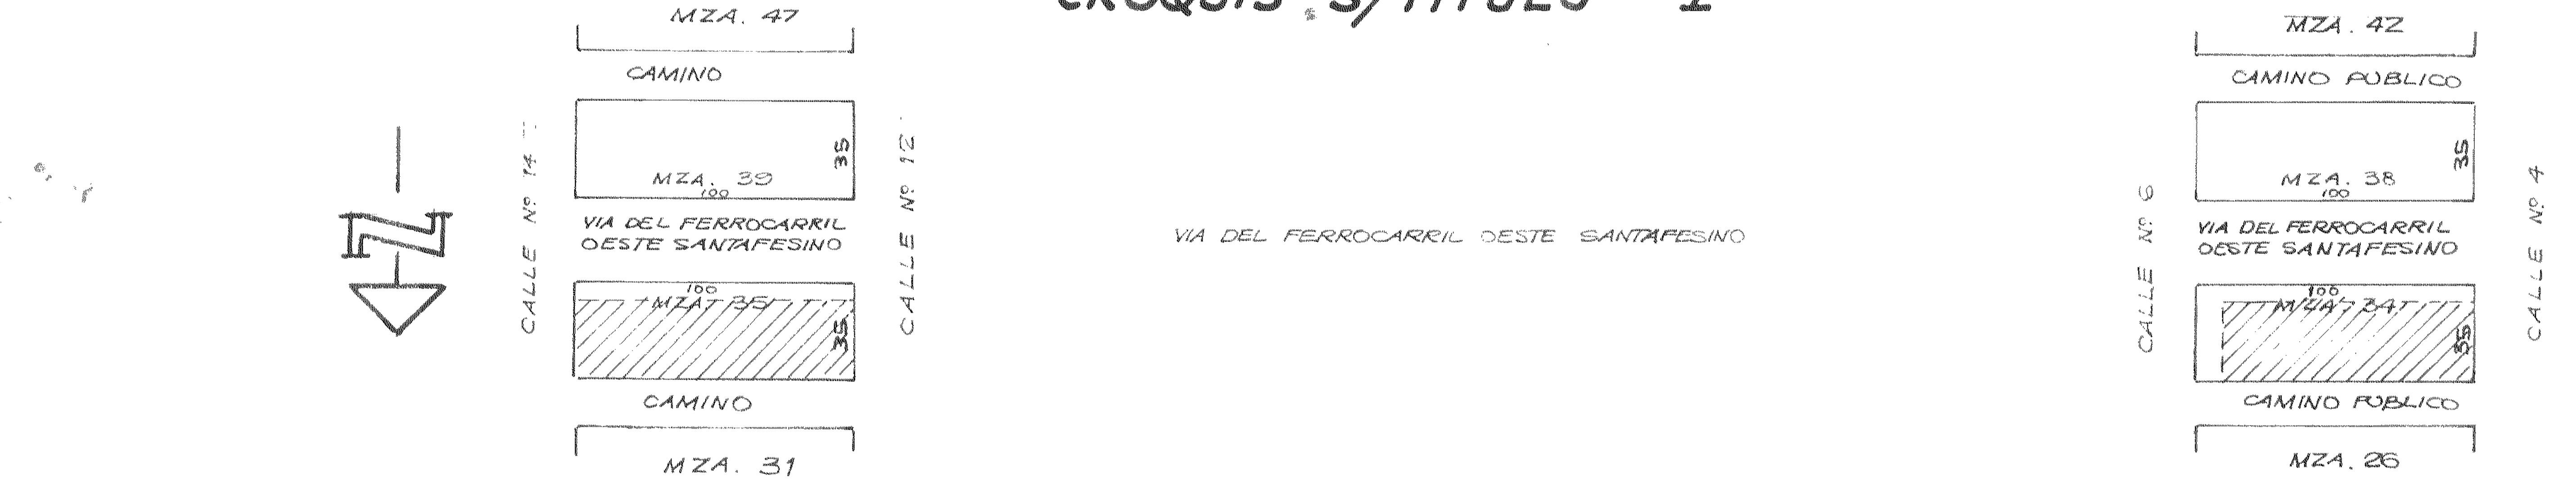
MZA. 47
CAMINO
MZA. 39
100
35
VIA DEL FERROCARRIL OESTE SANTAFESINO
MZA. 35
CAMINO
MZA. 31
CALLE Nº 14
CALLE Nº 12
VIA DEL FERROCARRIL OESTE SANTAFESINO
CALLE Nº 6
CALLE Nº 4
MZA. 42
CAMINO PUBLICO
MZA. 38
VIA DEL FERROCARRIL OESTE SANTAFESINO
MZA. 34
CAMINO PUBLICO
MZA. 26
N

## CROQUIS S/TITULO II

✻ SE TRANSFIEREN ACCIONES Y DERECHOS

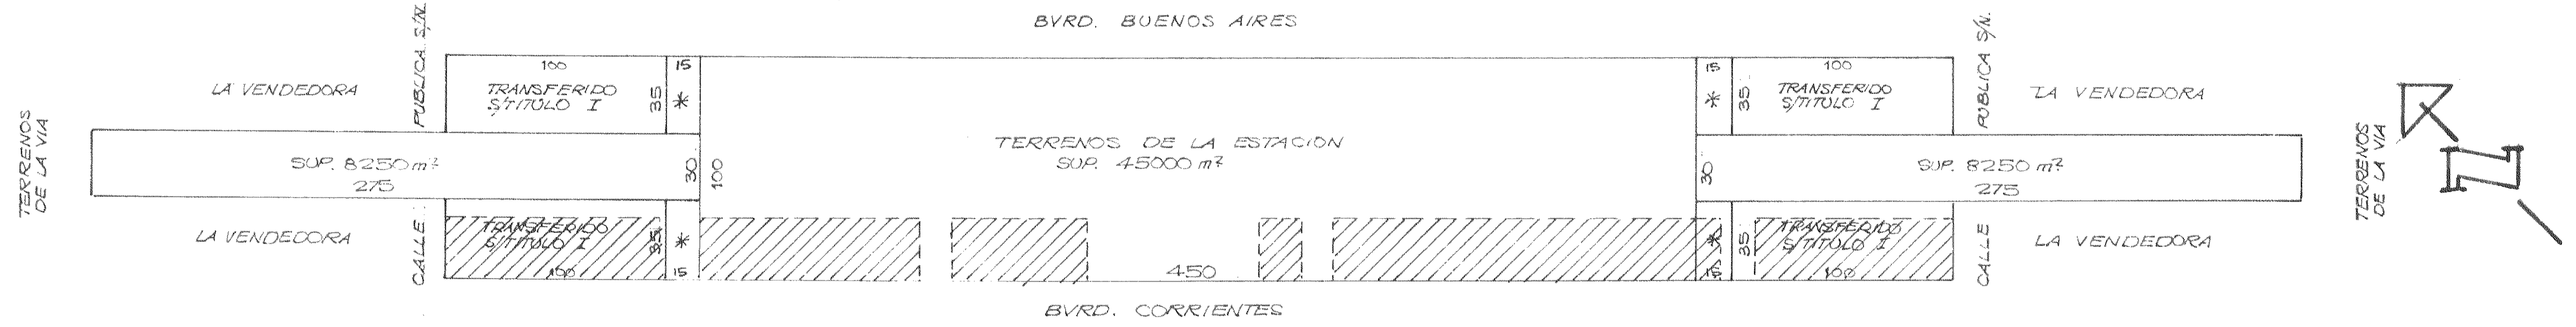
BVRD. BUENOS AIRES
TERRENOS DE LA VIA
LA VENDEDORA
PUBLICA S/N.
CALLE
TRANSFERIDO S/TITULO I
100
35
15
30
✻
SUP. 8250 m²
275
TERRENOS DE LA ESTACION
SUP. 45000 m²
100
450
BVRD. CORRIENTES
N

P.CIA. DE SANTA FE
DPTO. CASEROS
DTO. ARTEAGA
LUGAR: PUEBLO ARTEAGA

PLANO Nº

**P.I.I. Nº** NO FIGURA
AV. TERR. $ 695517.-
AÑO 1977

OBJETO
## MENSURA y SUBDIVISION

PROPIETARIO
# ESTADO NACIONAL ARGENTINO

INMUEBLE: UNA FRACCION DE TERRENO

**DOMINIO: Titulo I T° 5 F° 57 N° 1365** apart. 4° 14/2/1903
LEY NAC. Nº 13490 · PLANILLA SERIE $D_2$ Nº 84 · MARG. de TRANSF. Nº 100934 27/10/55

**Titulo II T° 5 F° 379 N° 13082** apart. 11° 5/10/1903
LEY NAC. Nº 13490 · PLANILLA SERIE $D_2$ Nº 84 · MARG. de TRANSF. Nº 100934 27/10/55

## BALANCE DE SUPERFICIES

| | | |
|---|---|---|
| SUPERFICIE S/TITULO I | (CALCULADA) | 14000,00 m² |
| " " II | (CALCULADA POR SUMA) | 61500,00 " |
| ∑ TOTAL S/TITULO | | 75500,00 m² |

**SUP. TOTAL LOTES S/M 14909,72 m²**
(SE EXCLUYE EL LOTE 14B)

## ACCIONES Y DERECHOS

SUPERFICIE S/TITULO II (CALCULADA) 2100,00 m²
SUP. LOTE 14B S/M 288,40 m²

**ING. GEOGR. ANA MARIA GURDULICH**
I.C.I. 6758 · 27 DE FEBRERO 349 · ROSARIO

ROSARIO, JULIO 1978

## OBSERVACIONES

ESCALA 1 : 1000  MEDIDAS EN METROS
Todos los ángulos son de 90°  Mojones de hierro en todos los vértices.
En el titulo I está errada la orientación.
En el titulo II se encuentran mal ubicados el Bv. Buenos Aires y Bv. Corrientes

El lote 14B se anexa al lote 14A y deberán ser transferidos conjuntamente.

## NOMENCL. CATASTRAL