



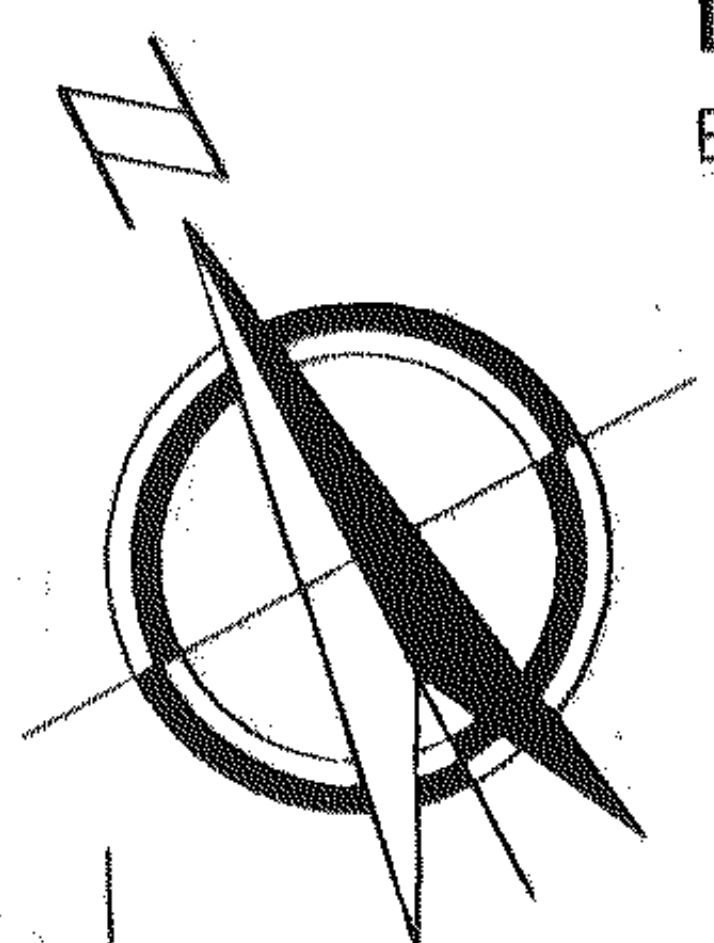

DETALLE DE MEJORAS

ESCALA 1 : 250

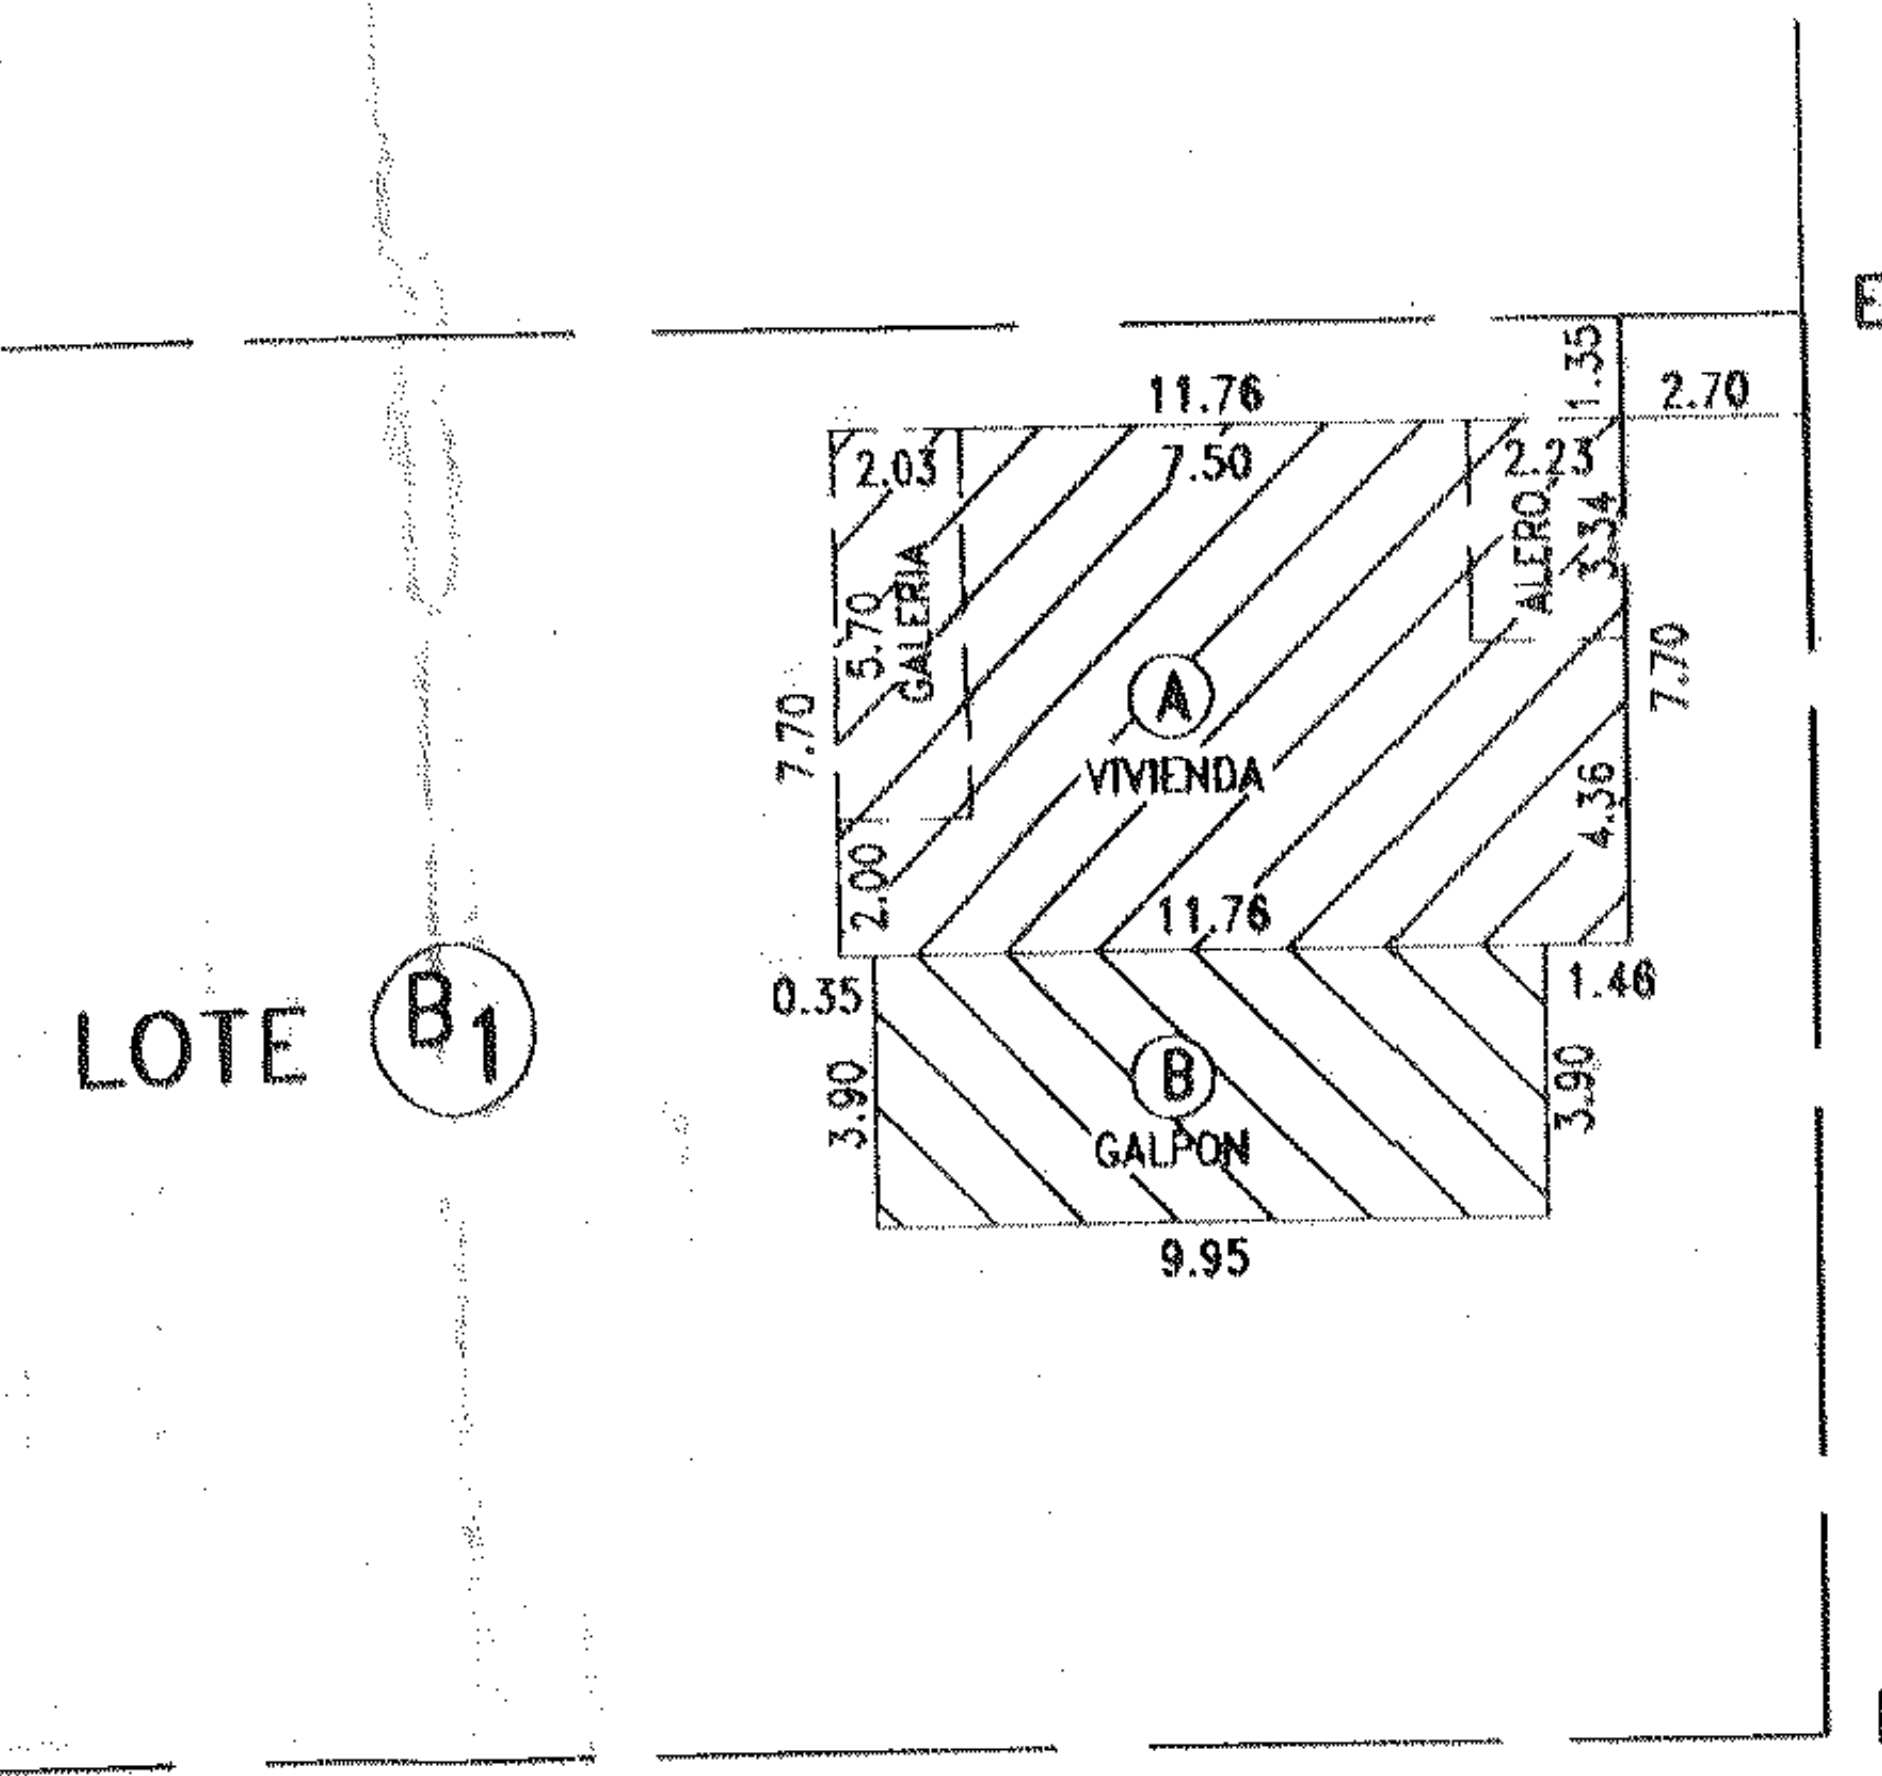

LOTE B1

[Signature]
FIRMA DEL PROPIETARIO
IRIS MARIA SABATTINI

COMPARACION DE SUPERFICIES

SUPERFICIE MEJORAS EMPADRONADAS: 000,0m²
SUPERFICIE MEJORAS EXISTENTES: 129,4m²
DIFERENCIA: 129,4m²


PLANILLA DE SUPERFICIES Y CATEGORIAS CATASTRALES DE LAS MEJORAS

LOTE	BLOQUE	PLANTA	SUPERFICIE	CATEGOR.	AÑO HABIL.	DESTINO	OBSERVACIONES
"B1"	A	BAJA	90,6m ²	7/3	1957	VIVIENDA	
	B	BAJA	38,8m ²	9/3	1957	GALPON	MAL ESTADO - FALTA TERMINACION
SUPERFICIE TOTAL EXISTENTE			129,4m ²				

INSTALACION SANITARIA COMPLETA: SI.
PAVIMENTO: SI, SOBRE CALLE VENEZUELA;
SOBRE BV.9S.AS.CORDON CUNETA.

SUPERFICIE DEMOLIDA SEGUN
DECLARACION PROPIETARIO:


ESCALA MENSURA 1:750 - ESCALA CALLES 1:750

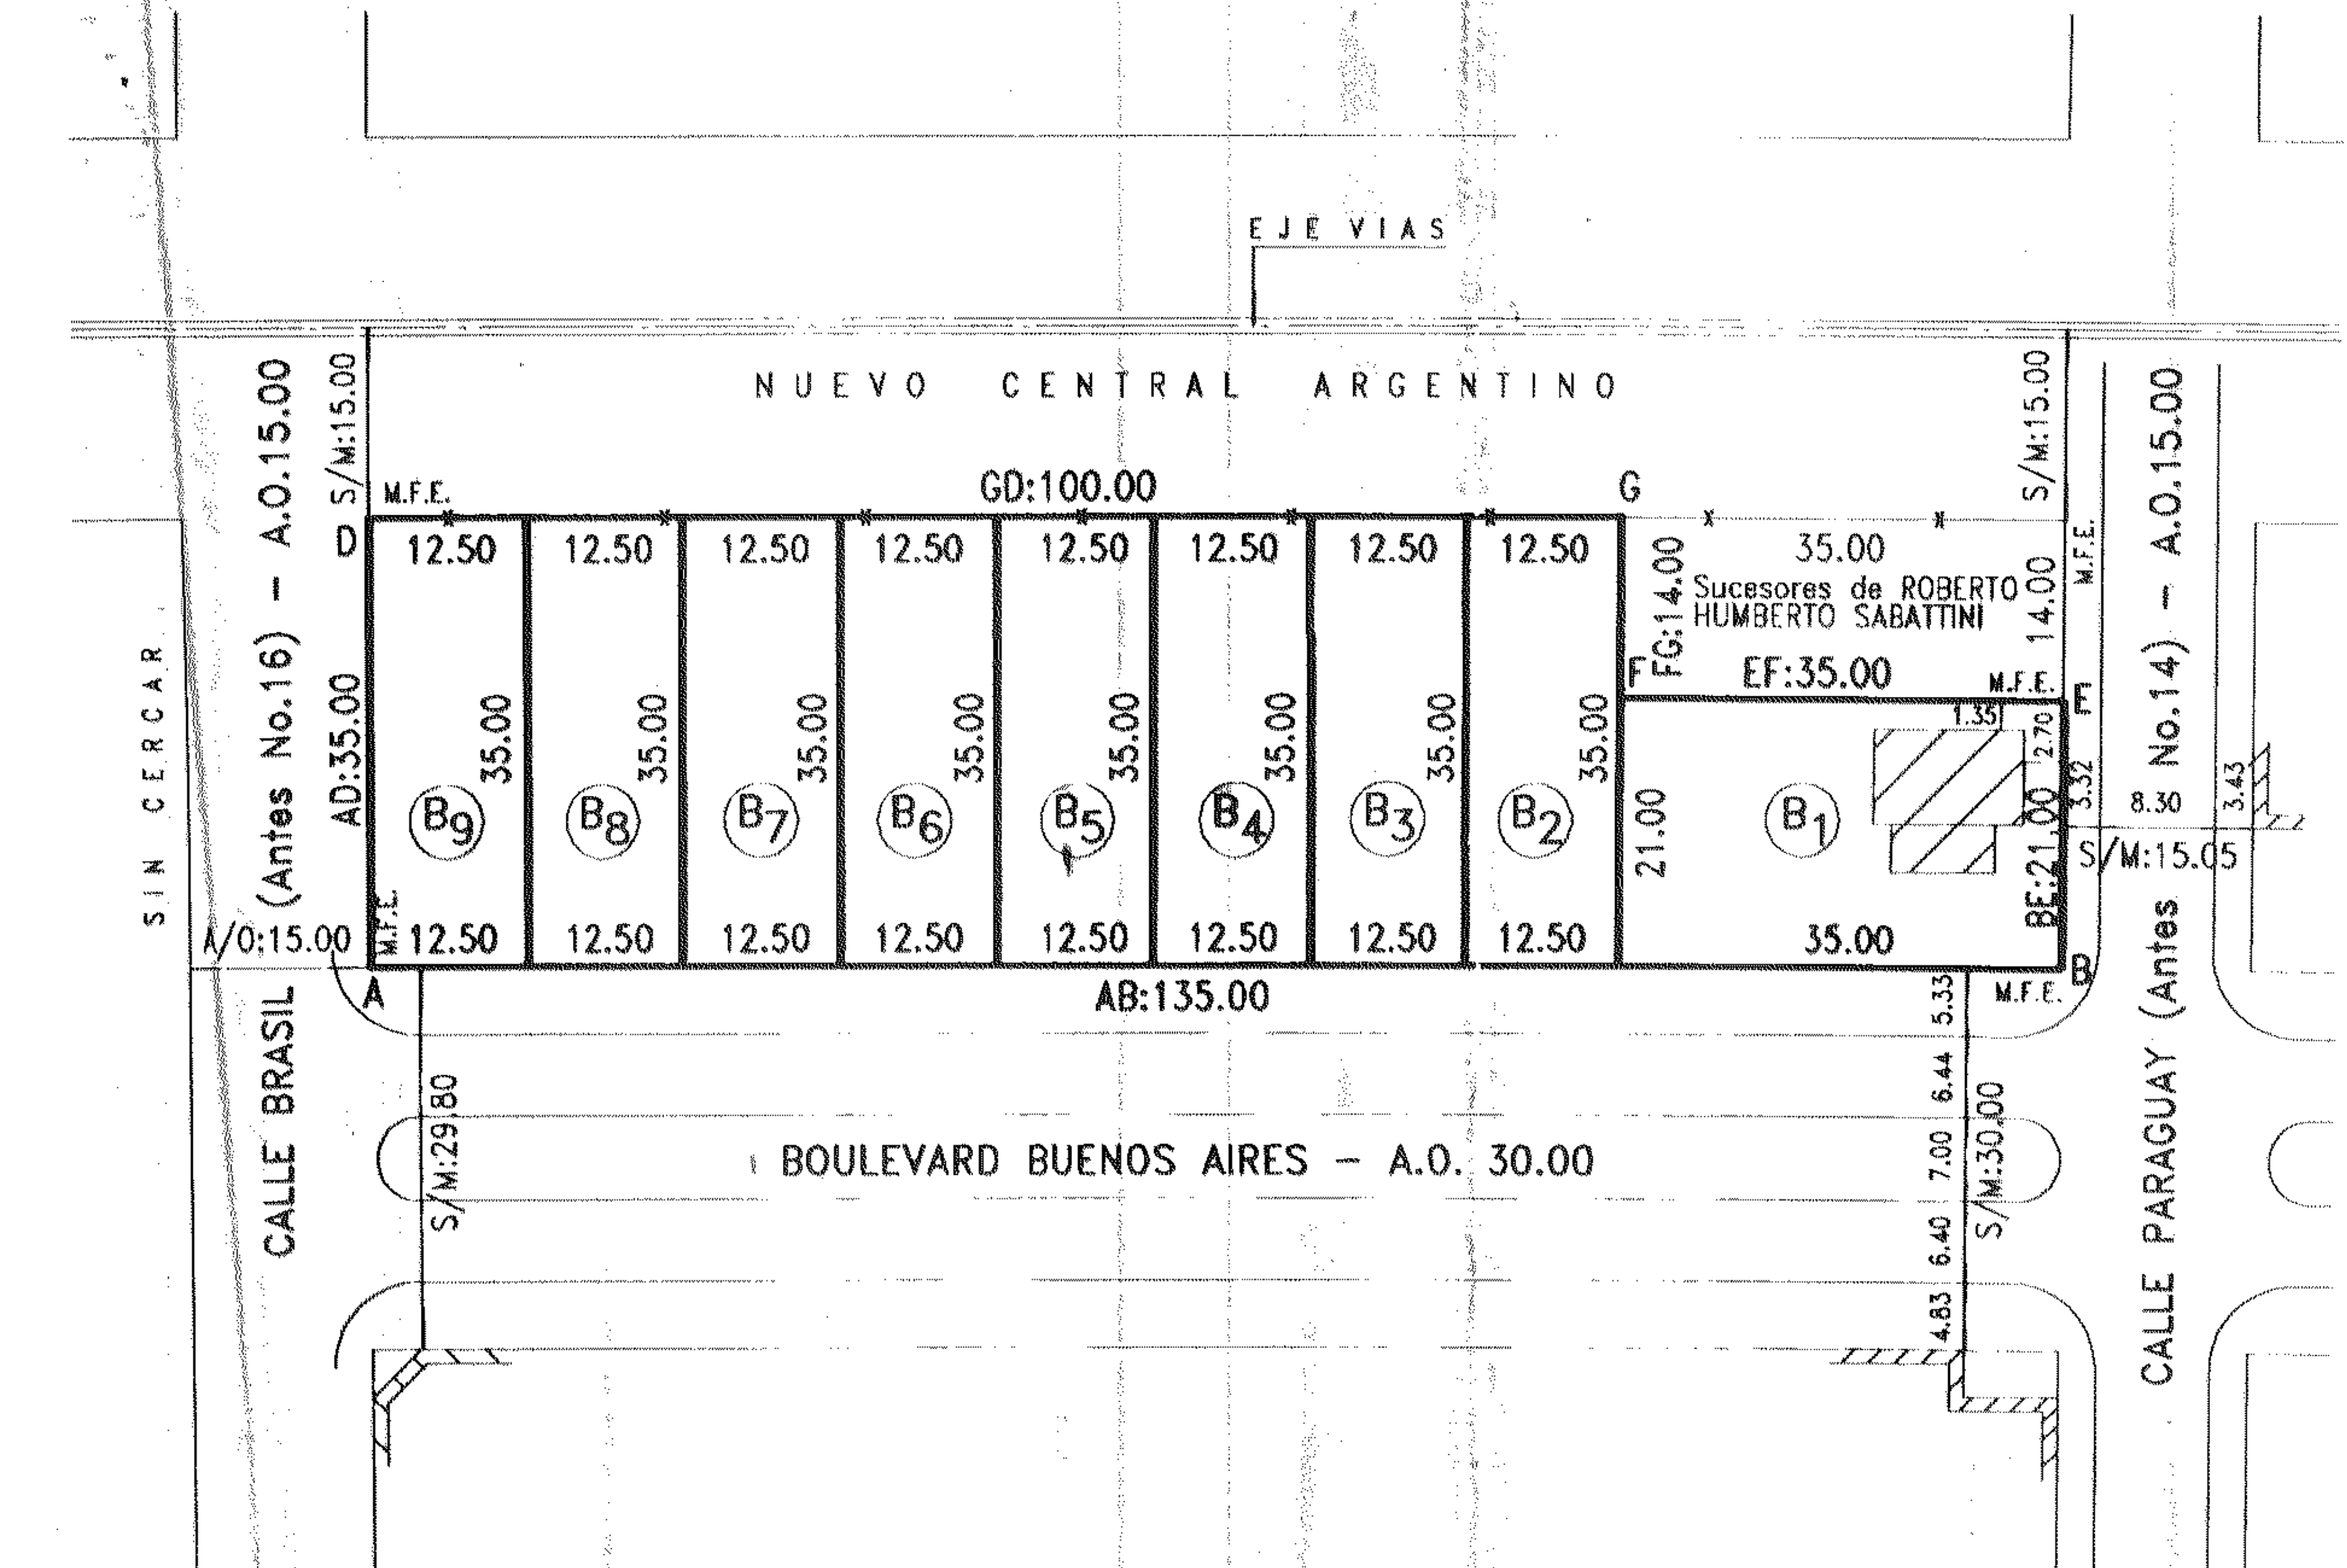

CROQUIS SEGUN TITULO

ESCALA 1 : 1.000



VIAS DEL FERROCARRIL CENTRAL ARGENTINO, HOY FERROCARRIL NACIONAL
GENERAL BARTOLOME MITRE.

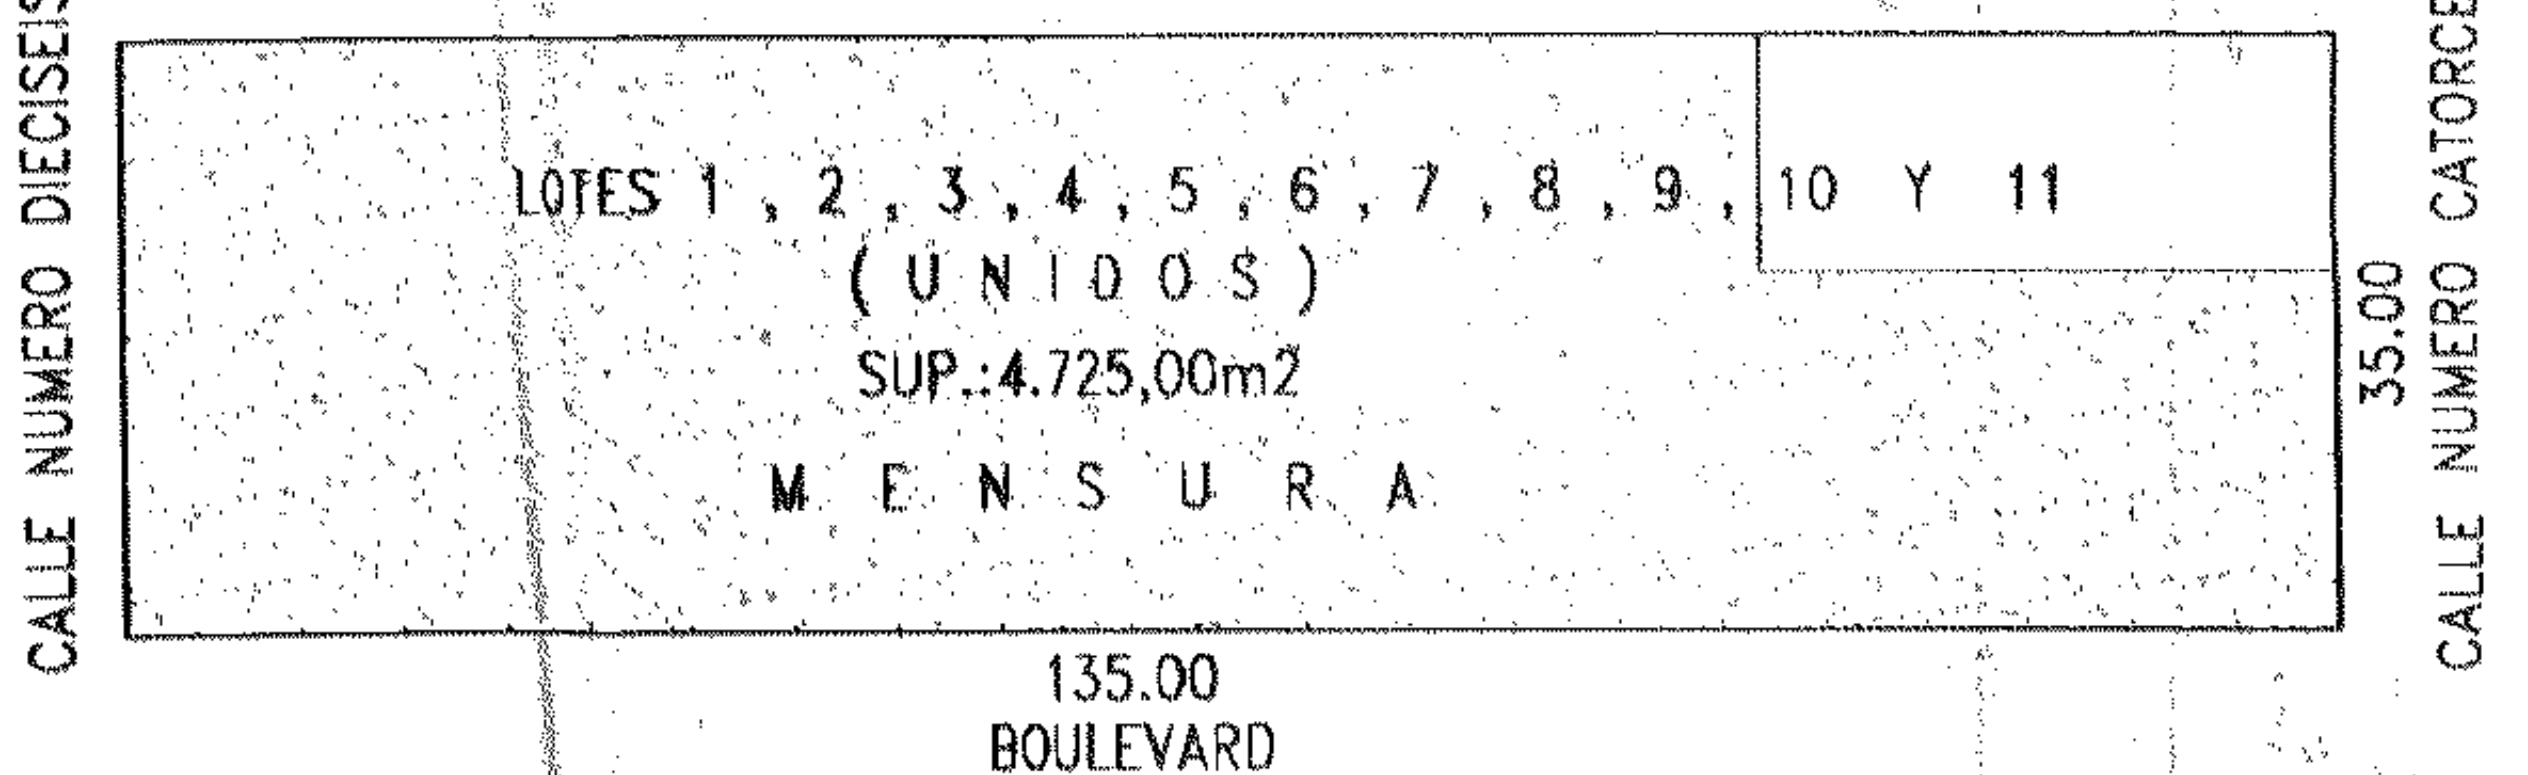

CROQUIS PLANO N°80.882/74

ESCALA 1 : 1.000

FERROCARRIL GENERAL BARTOLOME MITRE.

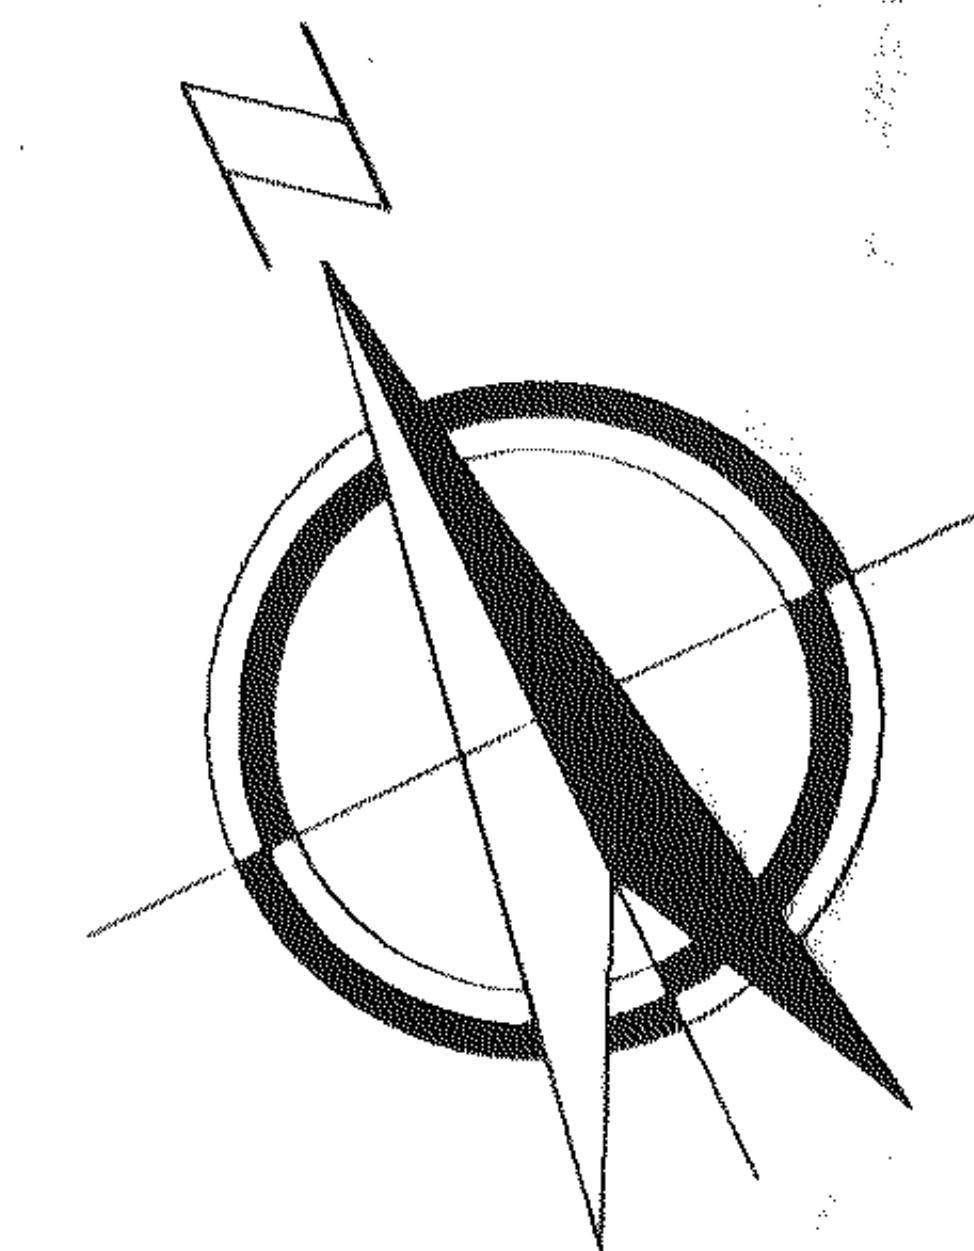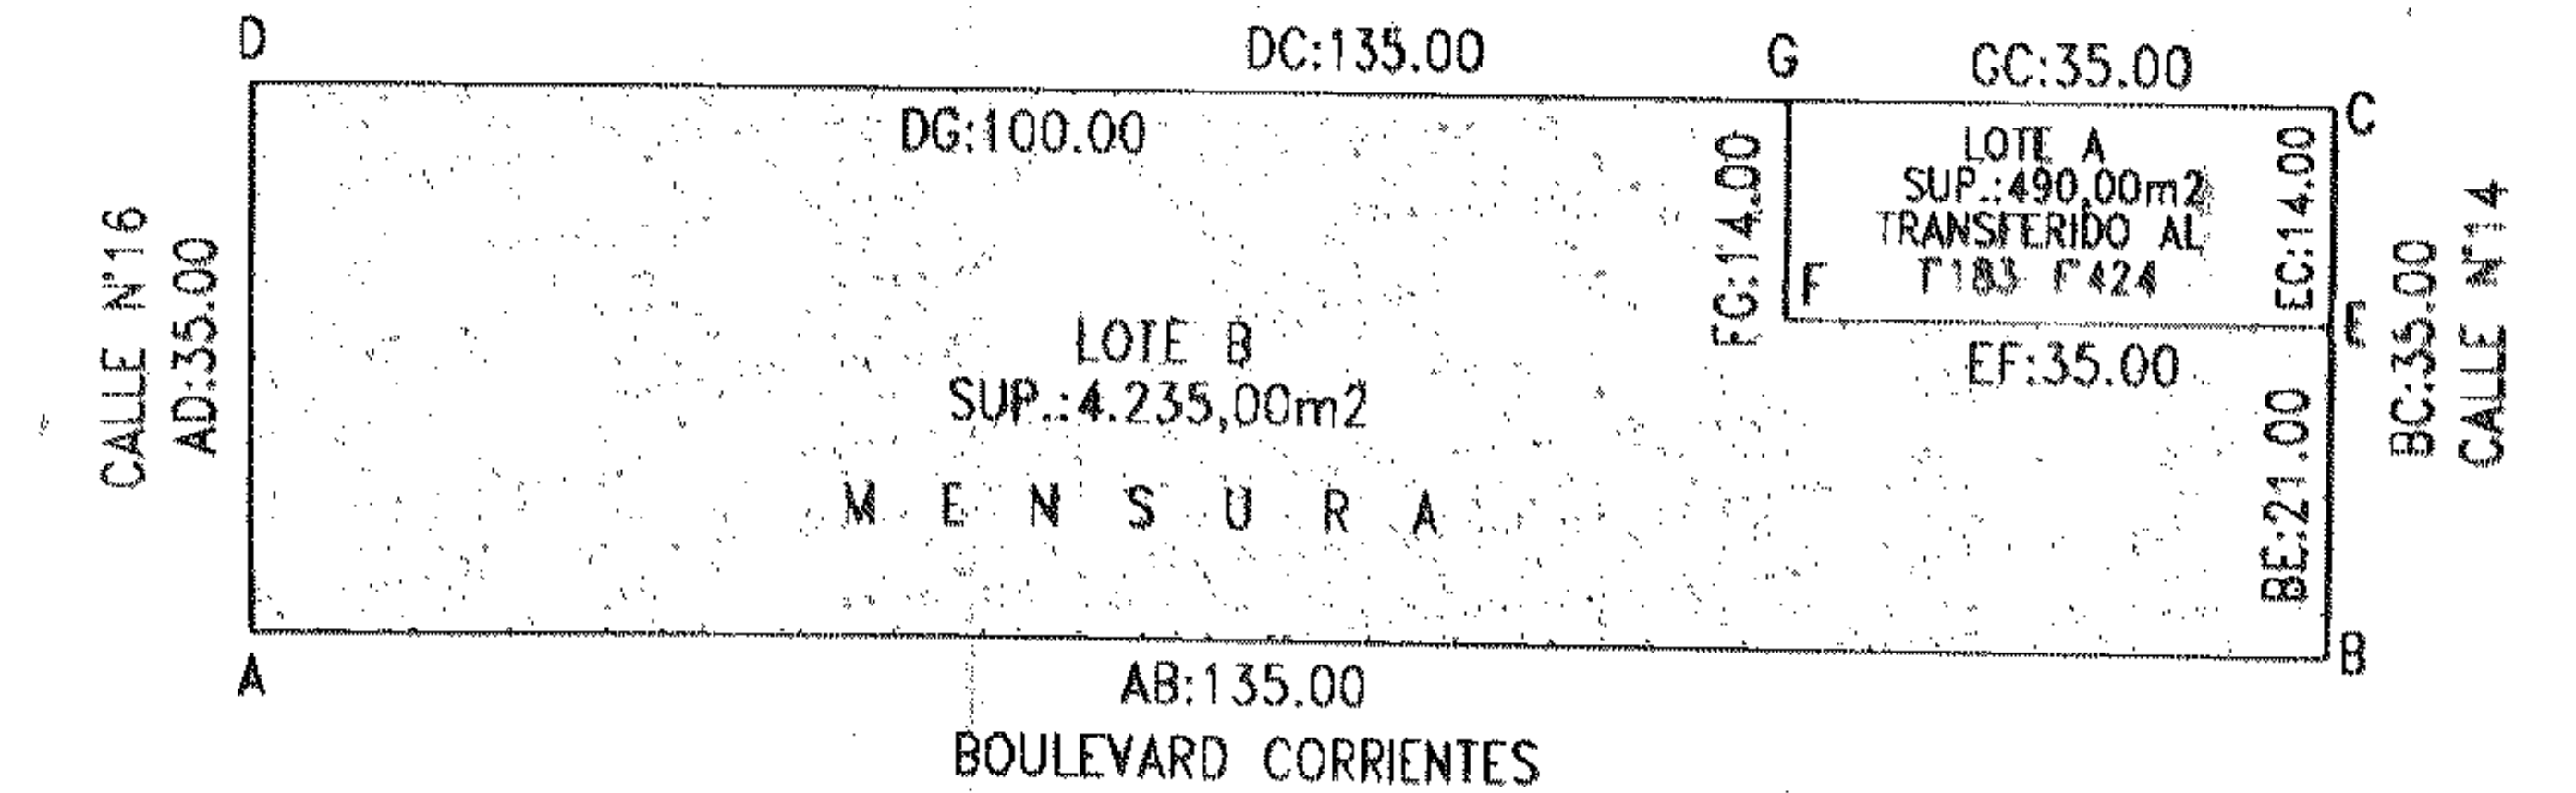

PROVINCIA DE SANTA FE
DEPARTAMENTO CASEROS
DISTRITO ARTEAGA
LUGAR PUEBLO ARTEAGA
MANZANA No.36

OBJETO: MENSURA Y SUBDIVISION

PROPIETARIO: **ROBERTO HUMBERTO SABATTINI.**(SUCESSION EN TRAMITE)

INMUEBLE: LOTE "B" DEL PLANO N°80.882/74 - MANZANA No.36.

DOMINIO: To.96-Fo.389-No.62.903-FECHA:01/04/57-DPTO.CASEROS.

BALANCE DE SUPERFICIES

SUPERFICIE SEGUN TITULO	4.725,00m ²
SUP.TRANSFERIDA(LOTE A-80.882/74)	490,00m ²
SUPERFICIE REMANENTE DE TITULO	4.235,00m ²
SUPERFICIE SEGUN MENSURA LOTE B1	735,00m ²
SUPERFICIE SEGUN MENSURA LOTE B2	437,50m ²
SUPERFICIE SEGUN MENSURA LOTE B3	437,50m ²
SUPERFICIE SEGUN MENSURA LOTE B4	437,50m ²
SUPERFICIE SEGUN MENSURA LOTE B5	437,50m ²
SUPERFICIE SEGUN MENSURA LOTE B6	437,50m ²
SUPERFICIE SEGUN MENSURA LOTE B7	437,50m ²
SUPERFICIE SEGUN MENSURA LOTE B8	437,50m ²
SUPERFICIE SEGUN MENSURA LOTE B9	437,50m ²
SUPERFICIE TOTAL SEGUN MENSURA	4.235,00m ²
DIFERENCIA	0,00m ²

[Signature]
ING.GEOG.ROBERTO O.S.DIAZ
ACO.P.A. No.2.0150.2
SAN MARTIN No.1971-CASILDA

CASILDA,NOVIEMBRE DE 1997.

OBSERVACIONES:

MEDIDAS LINEALES EXPRESADAS EN METROS - ANGULOS NO INDICADOS VALEN 90 GRADOS.
A.O. ANCHO OFICIAL - S/M SEGUN MENSURA - M.F.E. MOJON HIERRO EXISTENTE
M.F.C. MOJON HIERRO COLOCADO - M.M.E. MOJON MADERA EXISTENTE - (.)-ESTIMADO
REALICE PERSONALMENTE EL TRABAJO EL DIA 15/11/97.

NOMENCLATURA CATASTRAL

SECC.	POLIG.	MANZANA	PARC.	SUB.PARC.
		36	1	2

S.C.L.T. REG. CENAL
DEPARTAMENTO TOPOGRAFICO
13 ABR 1998
PLANO INSCRITO EN
N° 140857