142713/99

MENSURA: DETALLE DE MEJORAS
ESCALA 1 : 500

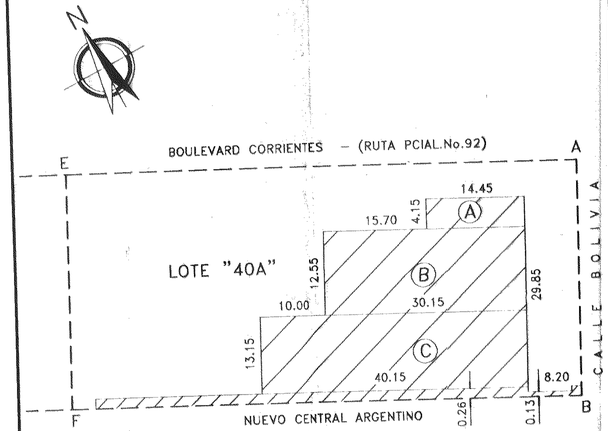

FIRMA DEL PROPIETARIO
SOC.TALLERES MARISA S.R.L.

COMPARACION DE SUPERFICIES

SUPERFICIE MEJORAS EMPADRONADAS: 416m2
SUPERFICIE MEJORAS EXISTENTES: 966m2
DIFERENCIA: 550m2

PLANILLA DE SUPERFICIES Y CATEGORIAS CATASTRALES DE LAS MEJORAS

LOTE	BLOQUE	PLANTA	SUP.CUB.	SUP.SEMICUB.	CATEGOR.	ANO HABIL.	DESTINO	OBSERVACIONES
40A	A	BAJA	59,97m2		6/2	1973	OFICINA	
	B	BAJA	378,38m2		9/2	1973	GALPON	
	C	BAJA	527,97m2		9/2	1975	GALPON	
SUPERFICIE TOTAL EXISTENTE			966,32m2					

SUPERFICIE DEMOLIDA SEGUN DECLARACION PROPIETARIO:

INSTALACION SANITARIA COMPLETA:
PAVIMENTO: SI.

ESCALA MENSURA 1 : 500 – ESCALA CALLES 1 : 750

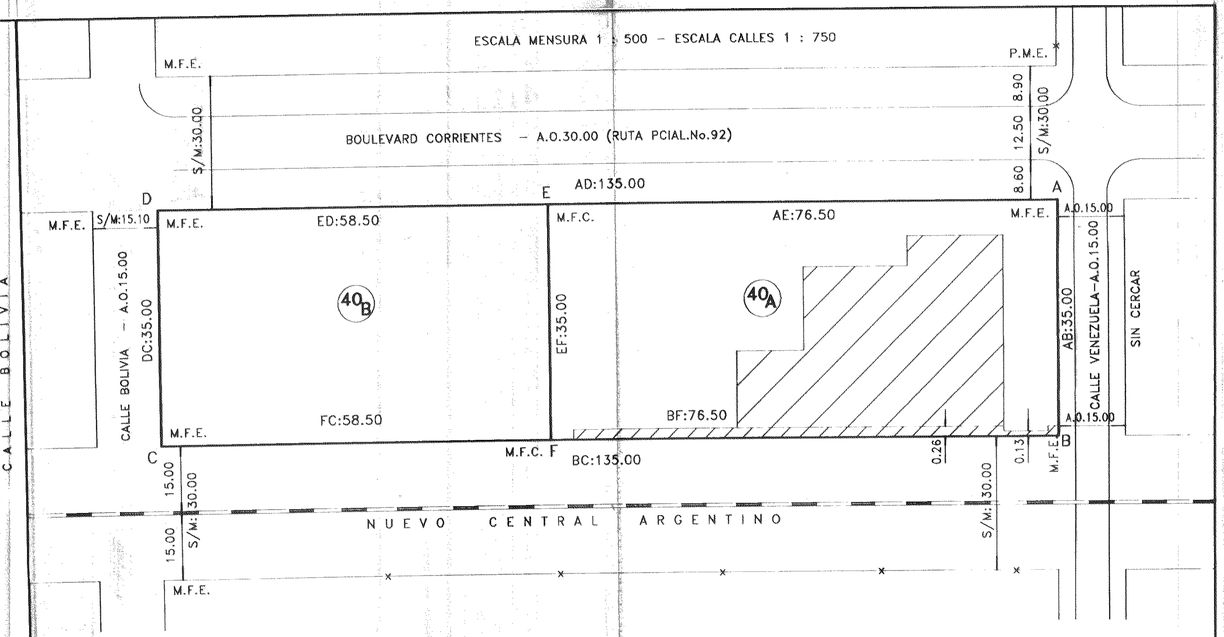

CROQUIS SEGUN TITULO
ESCALA 1 : 750

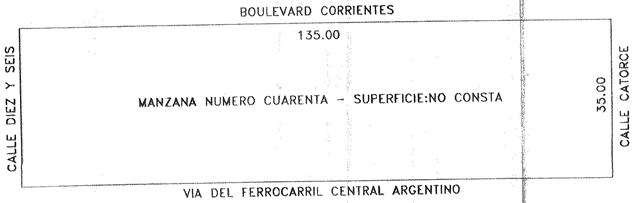

PROVINCIA DE SANTA FE
DEPARTAMENTO CASEROS
DISTRITO ARTEAGA
LUGAR PUEBLO ARTEAGA
MANZANA 40 – ZONA URBANA

PLANO No.: 142713
P.I.I.No.: 392.809/0000
AV.TERR.: $ 26.194,91/98.
AV.MEJ.: $54.448,62/98.

OBJETO: MENSURA Y SUBDIVISION

PROPIETARIO: SOCIEDAD "TALLERES MARISA S.R.L."

INMUEBLE: MANZANA NUMERO CUARENTA.

DOMINIO: To.:181–Fo.:92–No.:163.402–FECHA:16/09/74–DPTO.CASEROS.

BALANCE DE SUPERFICIES

SUPERFICIE SEGUN TITULO (CALCULADA) 4.725,00m2
SUPERFICIE SEGUN MENSURA LOTE "40A" 2.677,50m2
SUPERFICIE SEGUN MENSURA LOTE "40B" 2.047,50m2
SUPERFICIE TOTAL SEGUN MENSURA 4.725,00m2
Diferencia 0,00m2

ING.GEOG.ROBERTO O.S.DIAZ
I.CO.P.A. No.:2.0150.2
SAN MARTIN No.1971–CASILDA

CASILDA, ENERO DE 1999

OBSERVACIONES:

- MEDIDAS LINEALES EXPRESADAS EN METROS – M.F.E. MOJON HIERRO EXISTENTE.
- M.F.C. MOJON HIERRO COLOCADO – S/M SEGUN MENSURA.
- REALICE PERSONALMENTE EL TRABAJO EL DIA 04/01/99.
- ANGULOS NO INDICADOS MIDEN 90 GRADOS.

NOMENCLATURA CATASTRAL:

DPTO	DTO	SUB.DTO	Z
18	01	00	1

SECC.	POLIG.	MANZANA	PARC.	SUB.PARC.
		40	1	

S.C.I.T. REGIONAL ROSARIO
DEPARTAMENTO TOPOGRAFICO
29 JUN 1999
PLANO INSCRIPTO BAJO EL Nº. 142713