



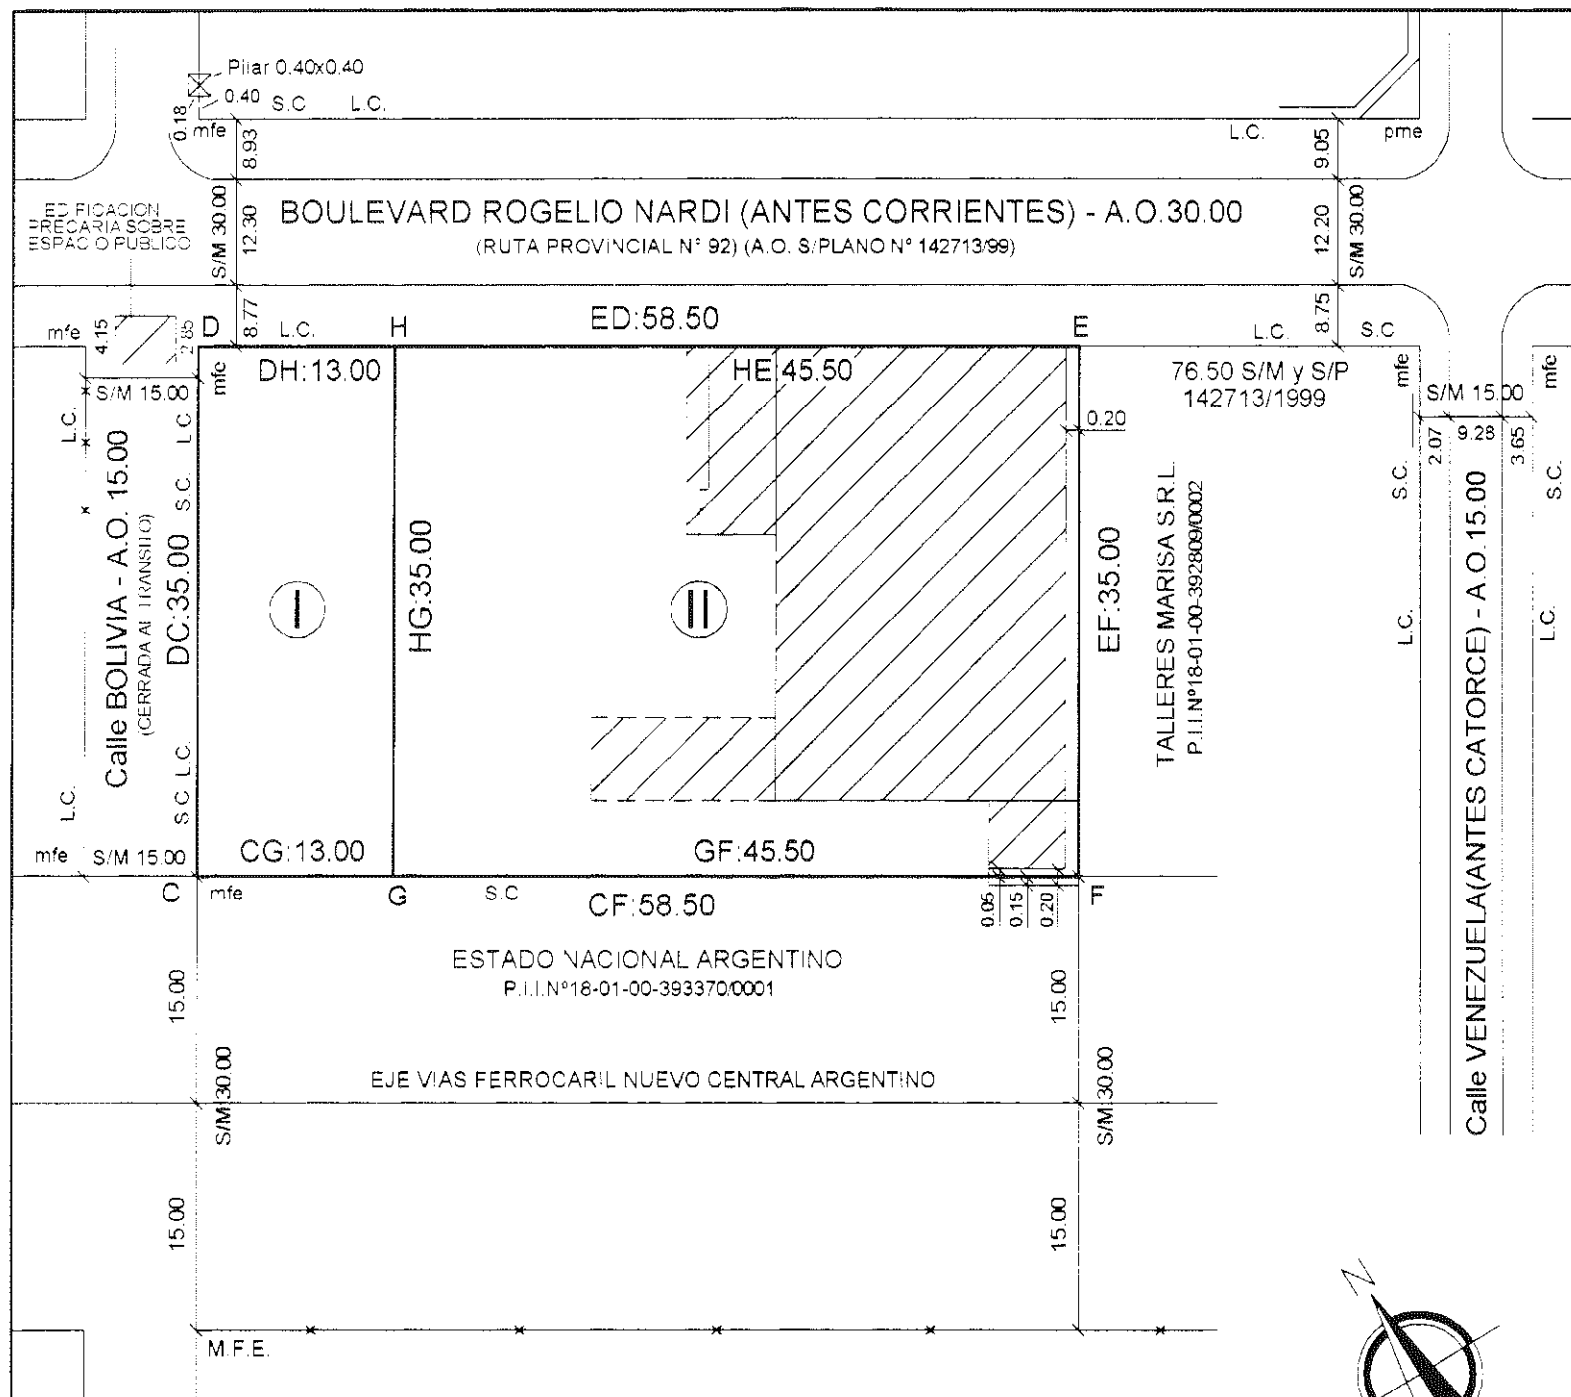

REPRESENTACION GRAFICA DE TITULO Y PLANO N°142713/1999  
ESCALA 1 : 750

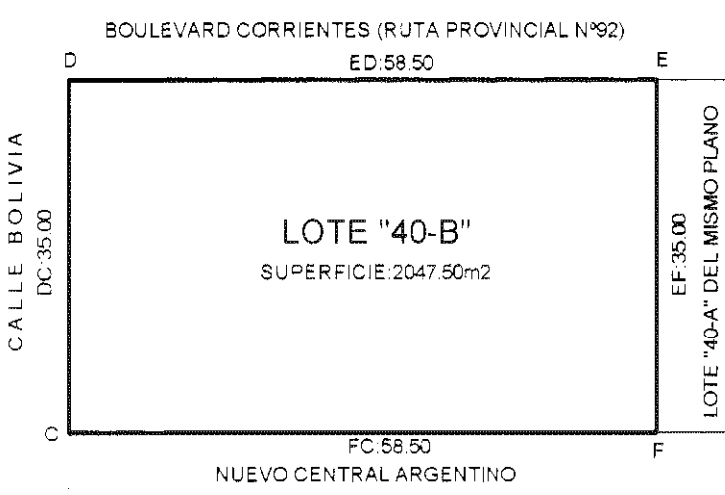

REFERENCIAS

|                                            |
|--------------------------------------------|
| ESCALA MENSURA 1 : 500                     |
| ESCALA CALLES 1 : 1000                     |
| MEDIDAS LINEALES EN METROS                 |
| MEDIDAS DE SUPERFICIES EN METROS CUADRADOS |
| ANGULOS NO INDICADOS M'DEN 90 o 270 GRADOS |
| L.C. LINEA COMUNAL - S.C. SIN CERCAR       |
| M.F.E. MOJON DE HIERRO EXISTENTE           |
| M.F.C. MOJON DE HIERRO COLOCADO            |
| P.V.E. POSTE MADERA EXISTENTE              |
| S/V SEGUN MENSURA                          |
| S/T SEGUN TITULO                           |
| A.O. ANCHO OFICIAL                         |
| S/P SEGUN PLANO                            |
| — LINEA DE ALAMBRADO                       |

|   |   |                                                         |
|---|---|---------------------------------------------------------|
| PLANO DE MENSURAS   |   | N° 208587                                               |
| PROVINCIA DE SANTA FE<br>DEPARTAMENTO: CASEROS<br>DISTRITO: ARTEAGA<br>LUGAR: PUEBLO ARTEAGA<br>MANZANA N°40 - ZONA URBANA                                                   |   | P.I.I.N° 392809/0001                                    |
| OBJETO: MENSURA Y SUBDIVISION   |   |                                                         |
| PROPIETARIOS: <b>FABIANA MARIEL CEGNA</b> (50%)<br><b>ARIEL PALMIRO CEGNA</b> (50%)                                                                                          |   |                                                         |
| INMUEBLES: MANZANA N°40 - LOTE "40-B" DEL PLANO N°142713/1999<br>DOMINIO: T°313 - F°457 - N°316949 - FECHA:03/03/2003 - DPTO.CASEROS                                         |   |                                                         |
| BALANCE DE SUPERFICIES ORIGINAL   |   |                                                         |
| SUPERFICIE SEGUN TITULO   |   | 2047.50m2                                               |
| SUPERFICIE LOTE "I" SEGUN MENSURA   |   | 455.00m2                                                |
| SUPERFICIE LOTE "II" SEGUN MENSURA   |   | 1592.50m2                                               |
| SUPERFICIE SEGUN MENSURA   |   | 2047.50m2                                               |
| DIFERENCIA   |   | 0.00m2                                                  |
| <br>ING. AGRIM. VERONICA PALOMA<br>I.C.O.P.A.N°2-0398/0<br>RIVADAVIA 1198-SAN JOSE DE LA ESQUINA<br>SAN JOSE DE LA ESQUINA, NOVIEMBRE DE 2017                                |   |                                                         |
| OBSERVACIONES:<br>-REALICE PERSONALMENTE EL TRABAJO EL DIA 13/10/2017<br>-VERTICES AMONONADOS CON HIERRO.<br>-VISADO EN LA DIRECCION PROVINCIAL DE VIALIDAD EN EXPEDIENTE N° |   |                                                         |
| <br>Arq. Alejandro Mogetta<br>Sr. de Planeamiento<br>COMUNA DE ARTEAGA   | NOMENCLATURA CATASTRAL<br>DPTO. DTO. SUBD. ZONA<br>18<br>SECC. POLIG. MANZANA<br>2<br>PARCELA SUBPARCELA<br>2 | <br>S.C.I.T.<br>14 FEB 2018<br>PLANO INSC.<br>N° 208587 |

